Светильник с поворотной консолью на трубном кронштейне Общий вид

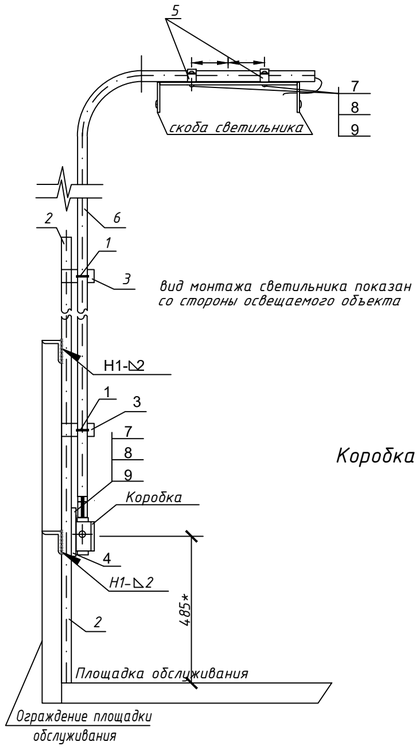

Опорная конструкция

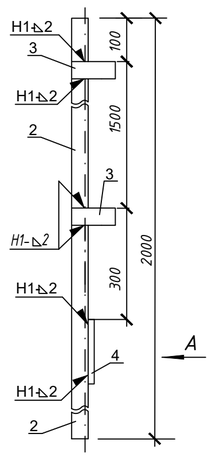

Поз.6 (Кронштейн)

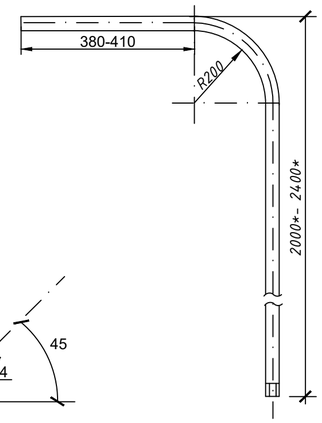

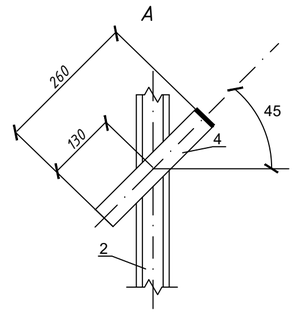

Коробка на опорной конструкции. Общий вид

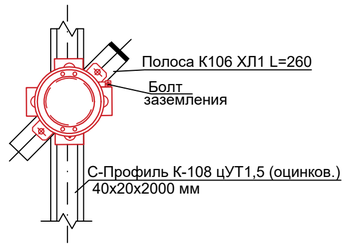

Поз.	Обозначение	Наименование	Кол.	Масса ед.,кг	Приме-чание
		Изделия ГЭМ на одну стойку и светильник			
1	ТУ36.18.00.01-49-89	Хомутик С438 Х-УТ2	2	0,06	
2	ТУ36-1434-82	С-Профиль К-108 цУТ1,5 (оцинков.) 40х20х2000 мм	1	1,25	
3	ТУ36-1434-82	Полоса К106 ХЛ1 L=100	2	0,144	
4	ТУ36-1434-82	Полоса К106 ХЛ1 L=260	1	0,250	
5	код 6040-32 (DKC)	Стальной хомут для труб 1" (32мм)	2		
		Материалы			
6	ГОСТ 3262-75	Труба 25х2,8	3	5.15	м
		Стандартные изделия			
7	ГОСТ 5915-70	Гайка М6-6Н.5(S10)	4	—	
8	ГОСТ 11371-78	Шайба А6.01.08кп.016	4	—	
9	ГОСТ 17473-80	Винт М6Х20.56.05	4	—	

Спецификация дана на лист.

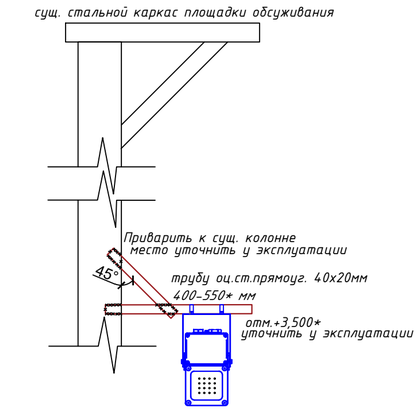

вид монтажа светильника показан со стороны освещаемого объекта

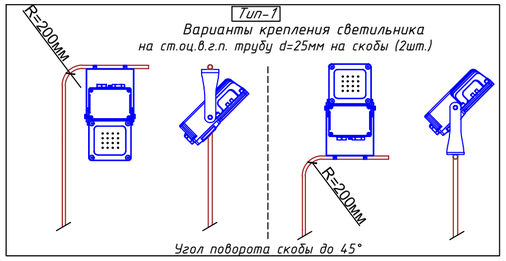

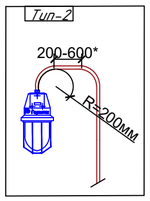

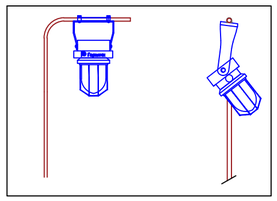

Эскиз заземления металлорукава

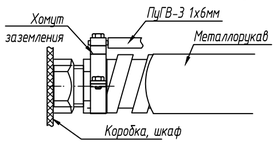

Эскиз монтажа заземляющего проводника на полосу заземления

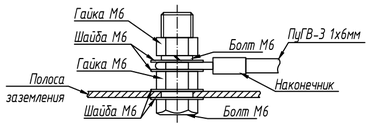

1. Сварные швы необходимо выполнить по ГОСТ 5264-80. Высоту сварного шва следует принять по наименьшей толщине сварных элементов, длину -по длине соприкосновения.
2. *Размеры для справки.
3. На чертеже даны основные узлы заземления.
4. Защитное заземление выполняется присоединением металлических корпусов электрооборудования, вводных коробок светильников к защитному нулевому PE-проводнику.
5. Заземление нетоковедущих корпусов электрооборудования, брони кабелей, кронштейнов светильников, труб электропроводки, металлорукавов, кабельных конструкций выполняется присоединением их к металлическим опорным конструкциям и к заземляющему устройству с помощью медного провода марки ПуГВ через болтовые соединения.
6. Способ и место присоединения заземляющих проводников к технологическому оборудованию принимаются согласно указаниям в конструкторской документации на оборудование и выполняются организацией, монтирующей это оборудование.
7. По окончанию работ по монтажу устройства заземления требуется заполнить акт скрытых работ.

Согласовано

Взам. инв. №

Подп. и дата

Инв. № подл.

Изм.	Кол.	Лист	N°док.	Подпись	Дата
Разраб.		Герлиц			12.2024
Н. контр.		Хабеев			12.2024
ГИП		Хабеев			12.2024

025-0221/24-ЭН

Реконструкция сети освещения в цехе №1 ЭЛОУ АВТ-7 НПЗ АО "ТАИФ-НК"

Схема наружного освещения

Стадия	Лист	Листов
Р	25	

Эскизы установки светильников. Заземление

ООО СтройЭкспертГрупп

Формат А2